

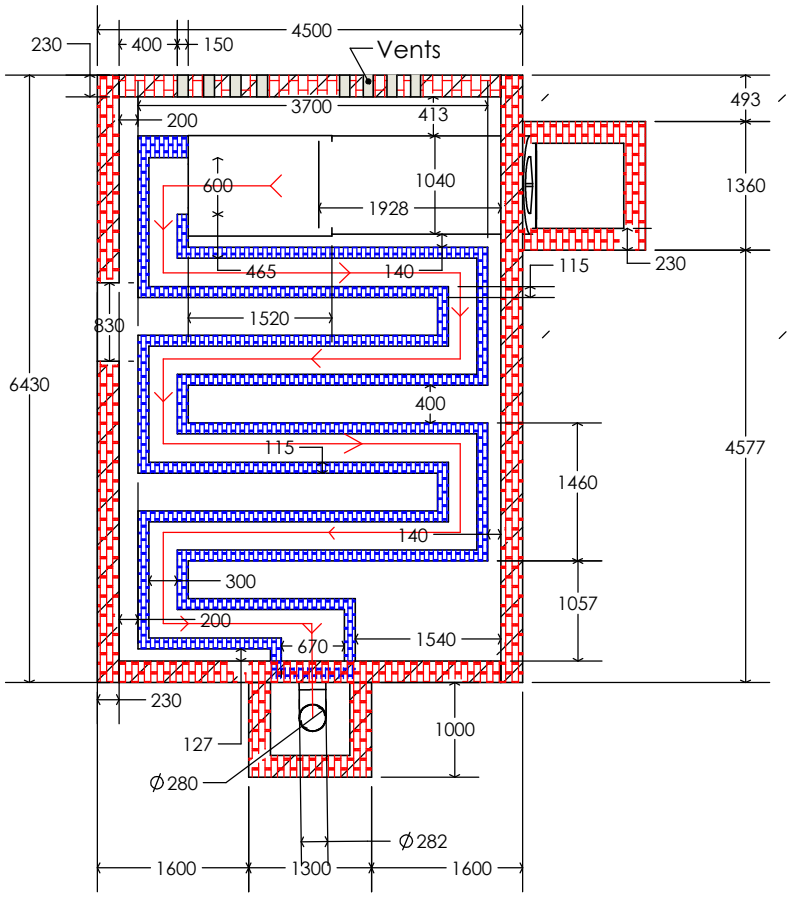



FLOOR PLAN
SCALE 1 : 80

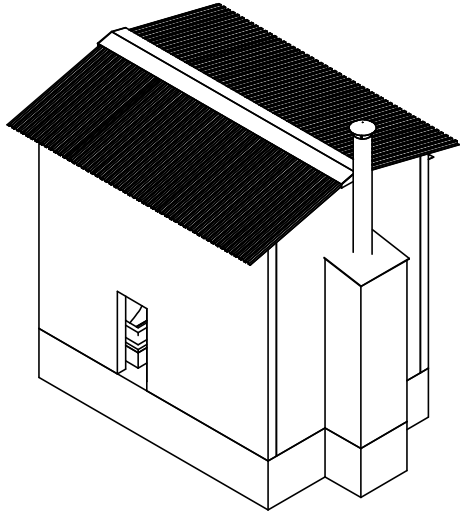

3D VIEW

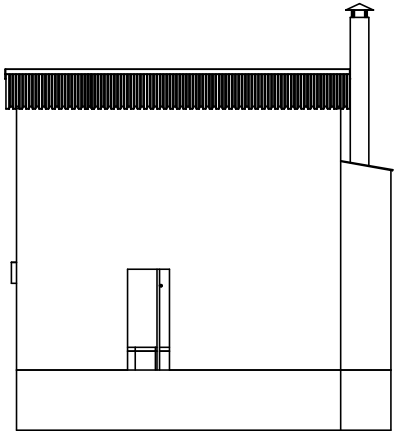



FRONT ELEVATION

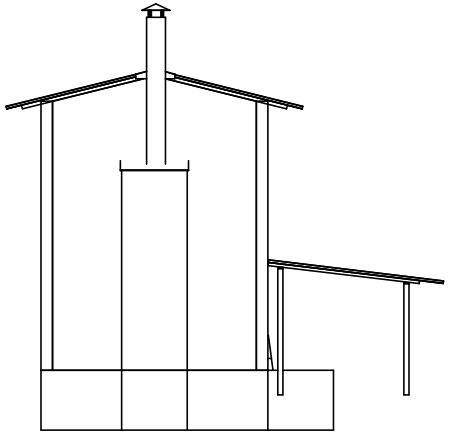

SIDE ELEVATION


TITLE: ROCKET BARN	IMPROVED BY: R. SILINGWANI	DATE: 20 JUNE 2025	DRG.No:
	CHECKED BY: T. MAGUSHU/O. MUDADISI	SCALE: 1:150	SHEET NO: 1
WEIGHT:	APPROVED BY: DR. M. NGWENYA	QTY:	SHEET SIZE : A4

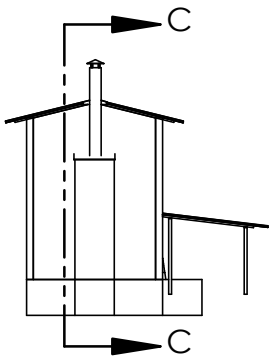


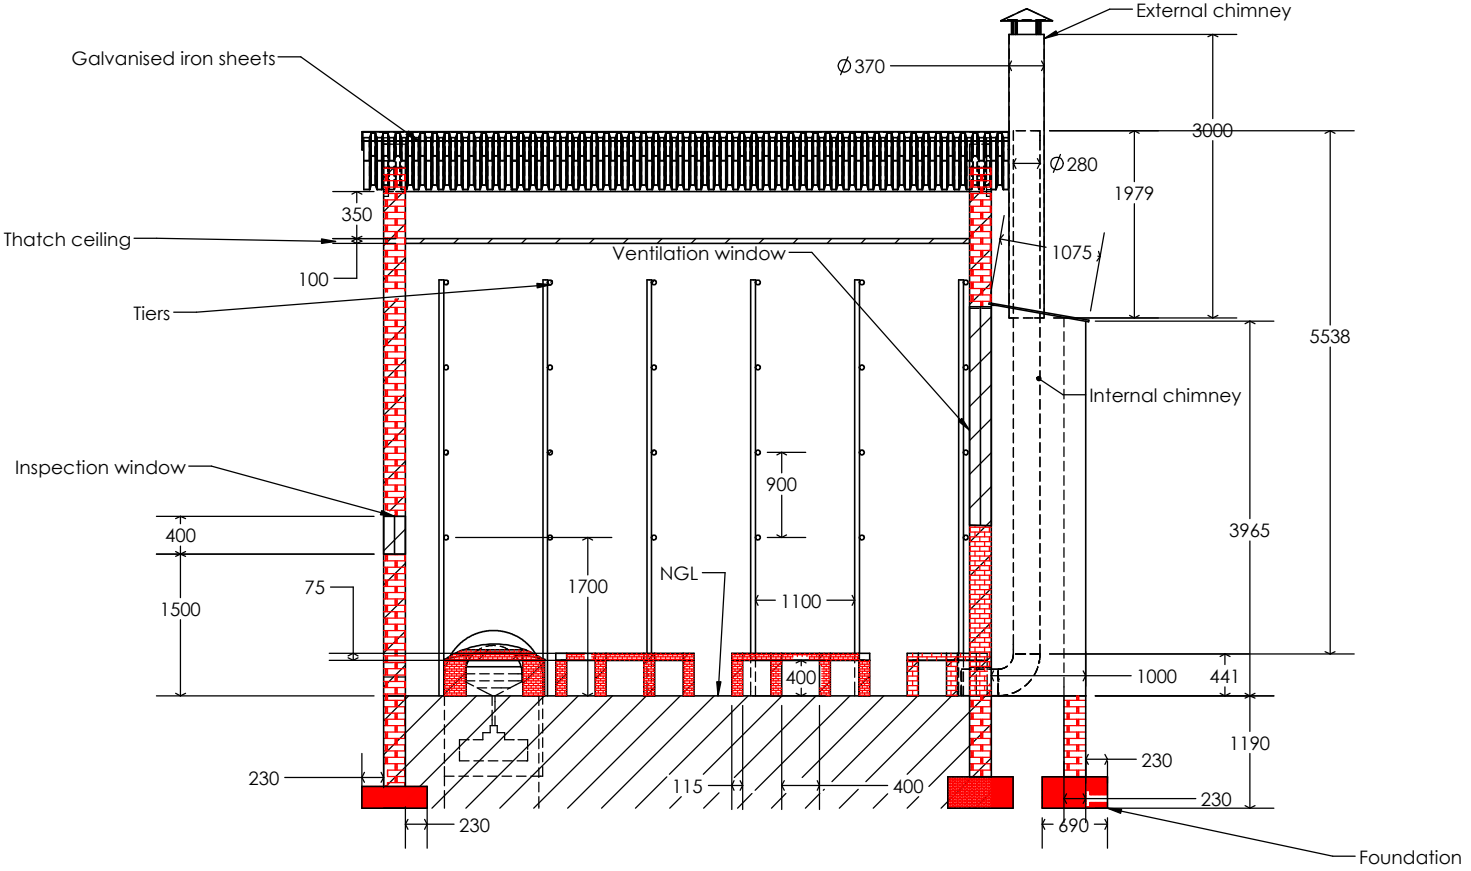

SECTION C-C
SCALE 1 : 80


TITLE: ROCKET BARN	IMPROVED BY: R. SILINGWANI	DATE: 20 JUNE 2025	DRG.No:
	CHECKED BY: T. MAGUSHU/ O. MUDADISI	SCALE: 1:150	SHEET NO: 2
WEIGHT:	APPROVED BY: DR. M. NGWENYA	QTY:	SHEET SIZE : A4

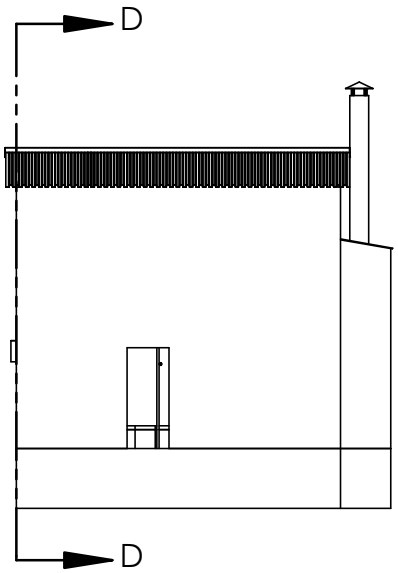


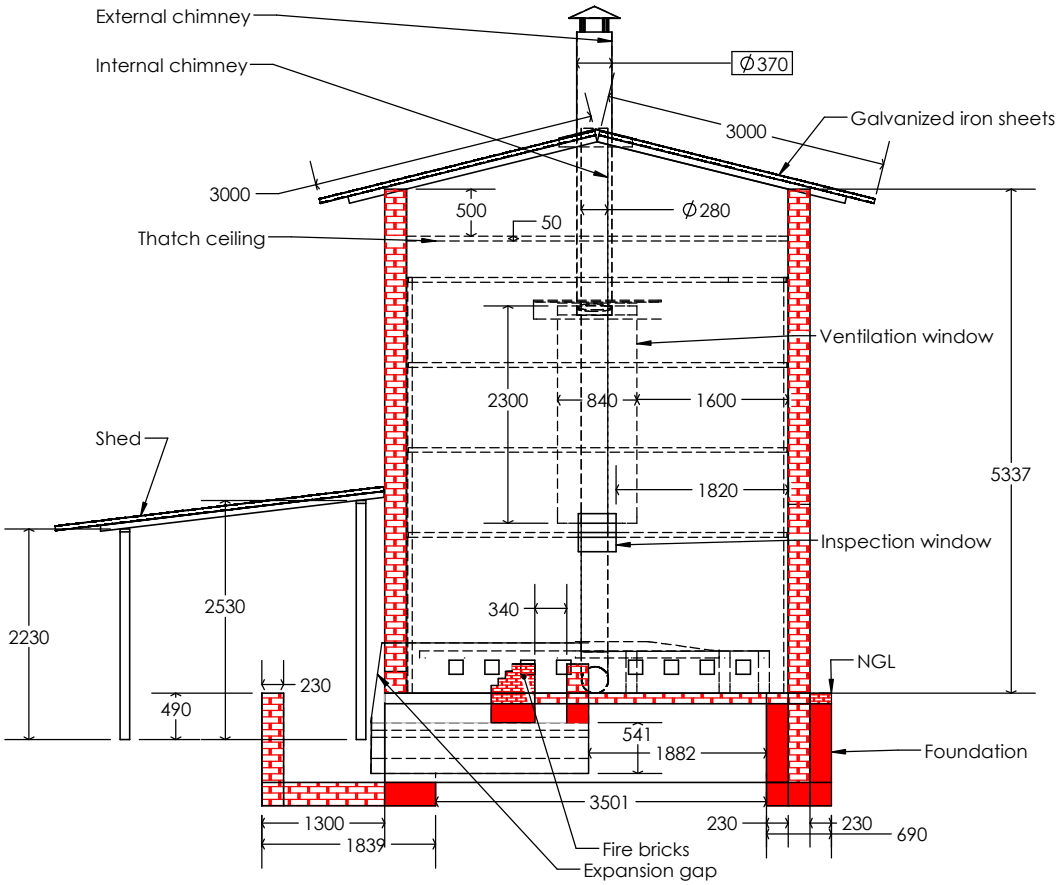



SECTION D-D
SCALE 1 : 80


TITLE: ROCKET BARN	IMPROVED BY: R. SILINGWANI	DATE: 20 JUNE 2025	DRG.No:
	CHECKED BY: T. MAGUSHU/ O. MUDADISI	SCALE: 1:150	SHEET NO: 3
WEIGHT:	APPROVED BY: DR. M. NGWENYA	QTY:	SHEET SIZE : A4

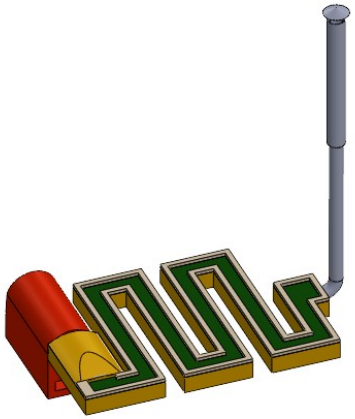

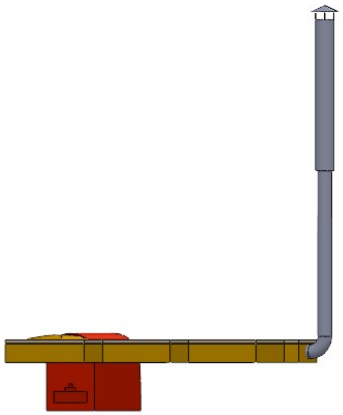

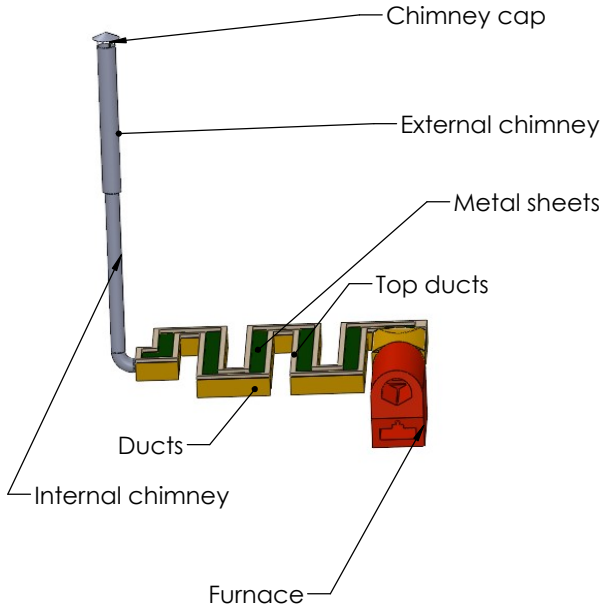

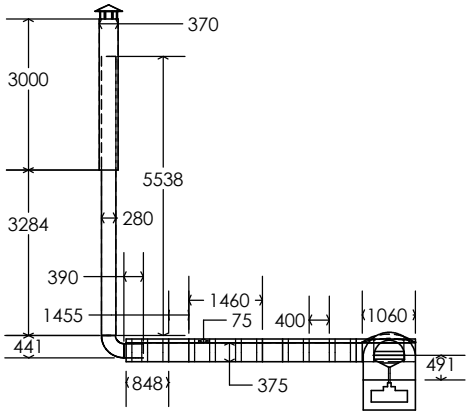


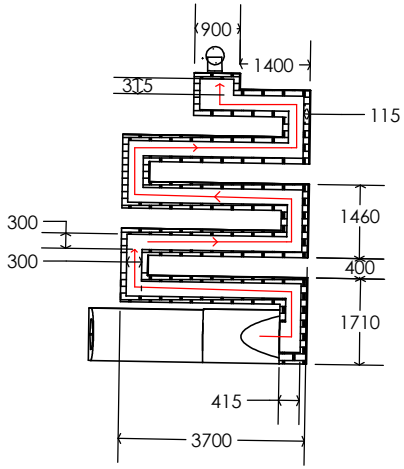



HEAT EXCHANGER

TITLE: ROCKET BARN	IMPROVED BY: R. SILINGWANI	DATE: 20 JUNE 2025	DRG.No:
	CHECKED BY: T. MAGUSHU/ O. MUDADISI	SCALE: 1:150	SHEET NO: 4
WEIGHT:	APPROVED BY: DR. M. NGWENYA	QTY:	SHEET SIZE : A4


FURNACE AND VENTS

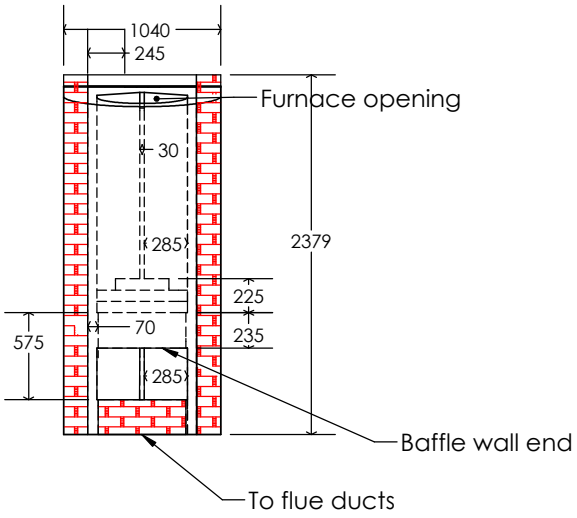


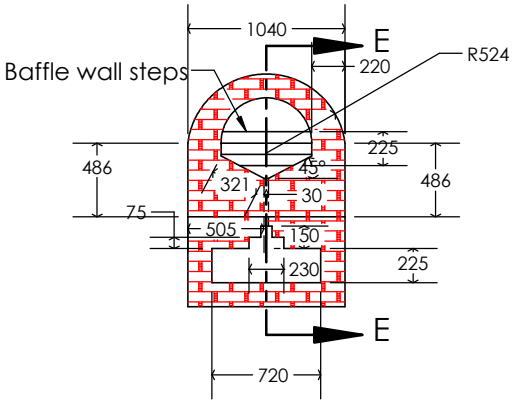


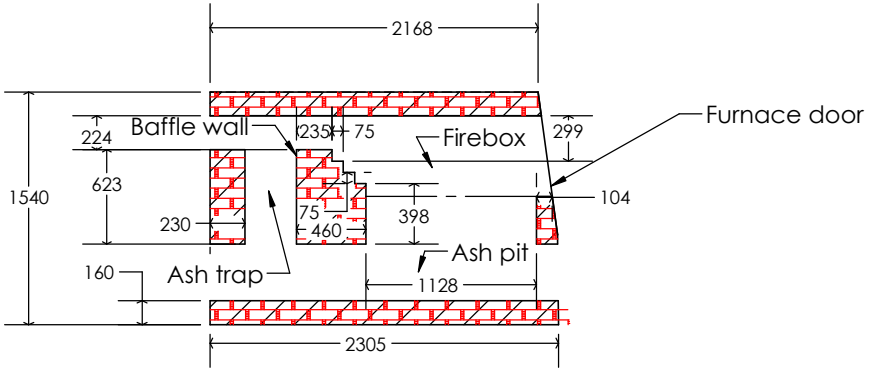

SECTION E-E

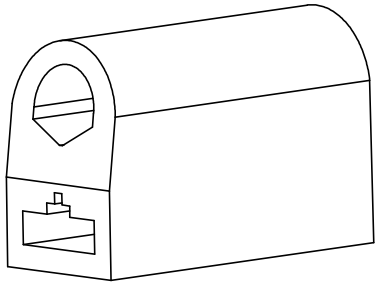


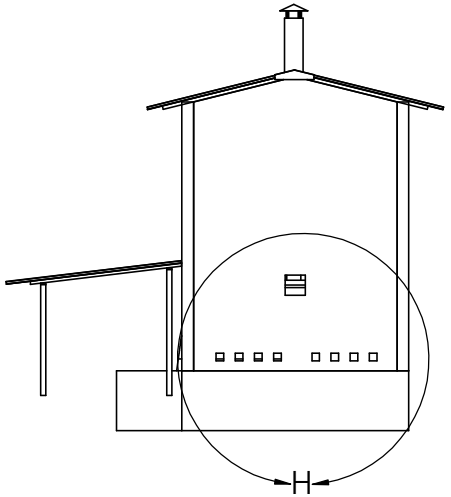


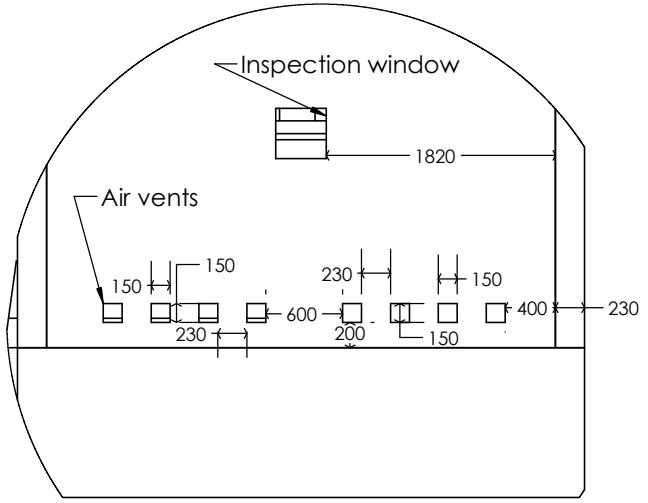



DETAIL H
SCALE 1 : 60


TITLE: ROCKET BARN	IMPROVED BY: R. SILINGWANI	DATE: 20 JUNE 2025	DRG.No:
	CHECKED BY: T. MAGUSHU/ O. MUDADISI	SCALE: 1:50	SHEET NO: 5
WEIGHT:	APPROVED BY: DR. M. NGWENYA	QTY:	SHEET SIZE : A4

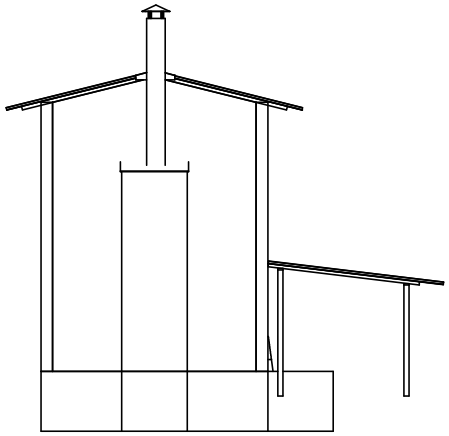


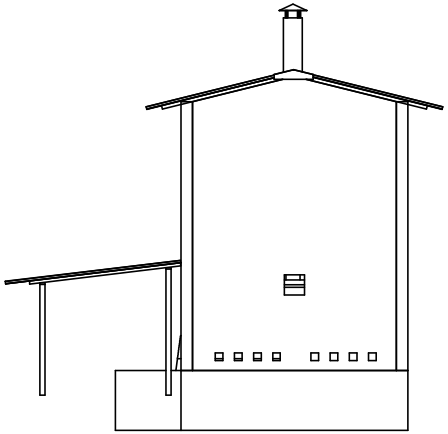

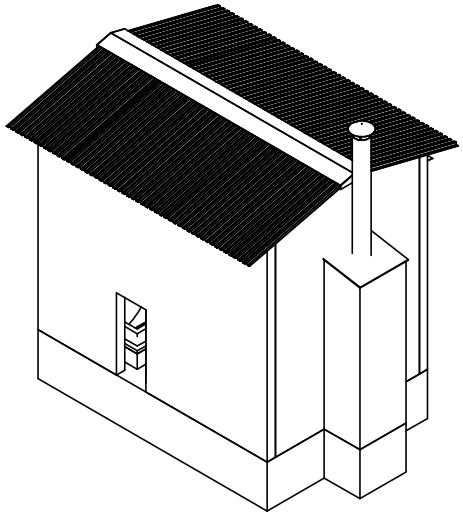

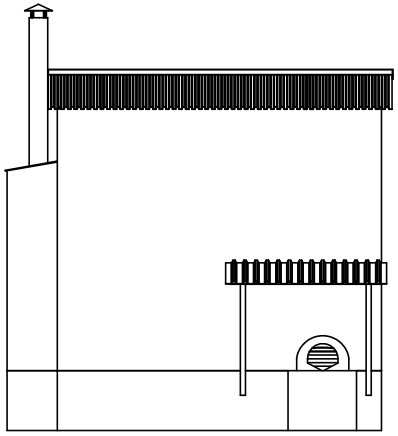

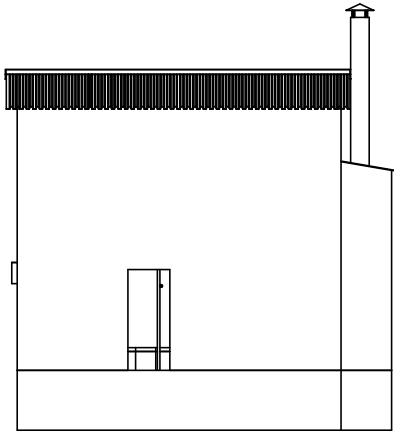

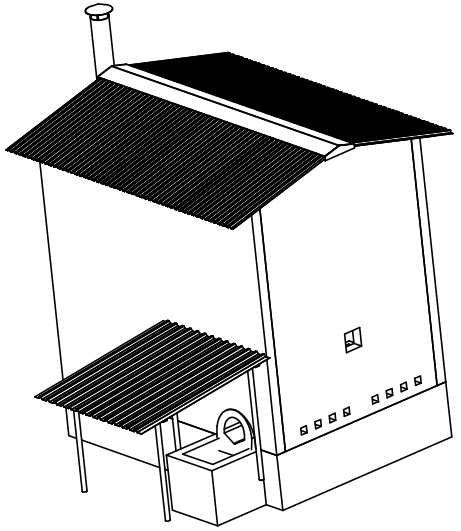

TITLE: ROCKET BARN	IMPROVED BY: R. SILINGWANI	DATE: 20 JUNE 2025	DRG.No:
	CHECKED BY: T. MAGUSHU/ O. MUDADISI	SCALE: 1:150	SHEET NO: 6
WEIGHT:	APPROVED BY: DR. M. NGWENYA	QTY:	SHEET SIZE : A4

BILL OF QUANTITIES

ITEM NO.	DESCRIPTION	UNIT	QUANTITY
1	PC 15 cement	50kg	22
2	Farm bricks (230mmx11mm5x75mm)	each	15000
3	9" brick force	roll	36
4	Pit sand	50kg	132
5	Antihill soil	50kg	220
6	**Heat exchanger** · 11' x 5400mm x 0.8mm thick flue pipe · 11' x 0.8mm thick flue pipe elbow · 14" x 2000mm x 0.8mm thick flue pipe · Fire bricks · 700mm x 700mm furnace door · Firebox 530mm x 1mm galvanized metal sheet · 1200mm x 1mm chimney metal plate/sheet	each each each each each 20m 1.2m	1 1 1 120 1 1 1
7	**Timber** 5 m long x 108mm diameter tiers	each	24
8	40mm x 40mm U-nails (8 gauge) Hooks	each each	600 800
9	Clips (Short - type talita) ***It is advisable to have another set of 467 clips to enable reaping while untying is taking place.***	each	467
10	**Ceiling** • Thatching grass(8mm thick) • 250 micron black plastic - 6 m x 6 m • 38mm brandering gum strip thatch holders -5m, spaced 30cm • 6mx150mm gum poles • 5m x 150 mm gum poles	each each each each each	6 1 20 22 3
11	**Roofing** • 75mmx38mm roofing timber • 2000mmx800mm door • 850mmx2000mm door frame Others • 250mmx 50mm timber for making lintels • 800mm x 3000mm roofing metal sheets (IBR) • 800mm x 2000mm foam rubber • Galvanized IBR top covers	6m each each each 3m each each each each	 6 1 1 1 18 1 9

KUTSAGA	TITLE: ROCKET BARN	IMPROVED BY: R. SILINGWANI	DATE: 20 JUNE 2025	DRG.No:
		CHECKED BY: T. MAGUSHU/ O. MUDADISI	SCALE: 1:150	SHEET NO: 7
	WEIGHT:	APPROVED BY: DR. M. NGWENYA	QTY:	SHEET SIZE : A4