


KUTSAGA ROCKET TUNNEL BARN


The Kutsaga Rocket Tunnel Barn (6–10 ha capacity) is designed for large-scale growers seeking high throughput without compromising curing quality. Built around a continuous-flow trolley system and the contour curing principle, it enables smooth material handling and efficient batch movement through the curing chamber. Powerful, controlled airflow combined with optimized fuel combustion ensures uniform heat distribution and consistent curing across large volumes of tobacco.

Its continuous operation reduces labour demand, improves temperature and humidity control, and minimizes defects such as green spots, case hardening, and colour variation. By enhancing fuel efficiency and increasing seasonal throughput, the system delivers significant cost savings,


KUTSAGA
For Productivity. For Sustainability

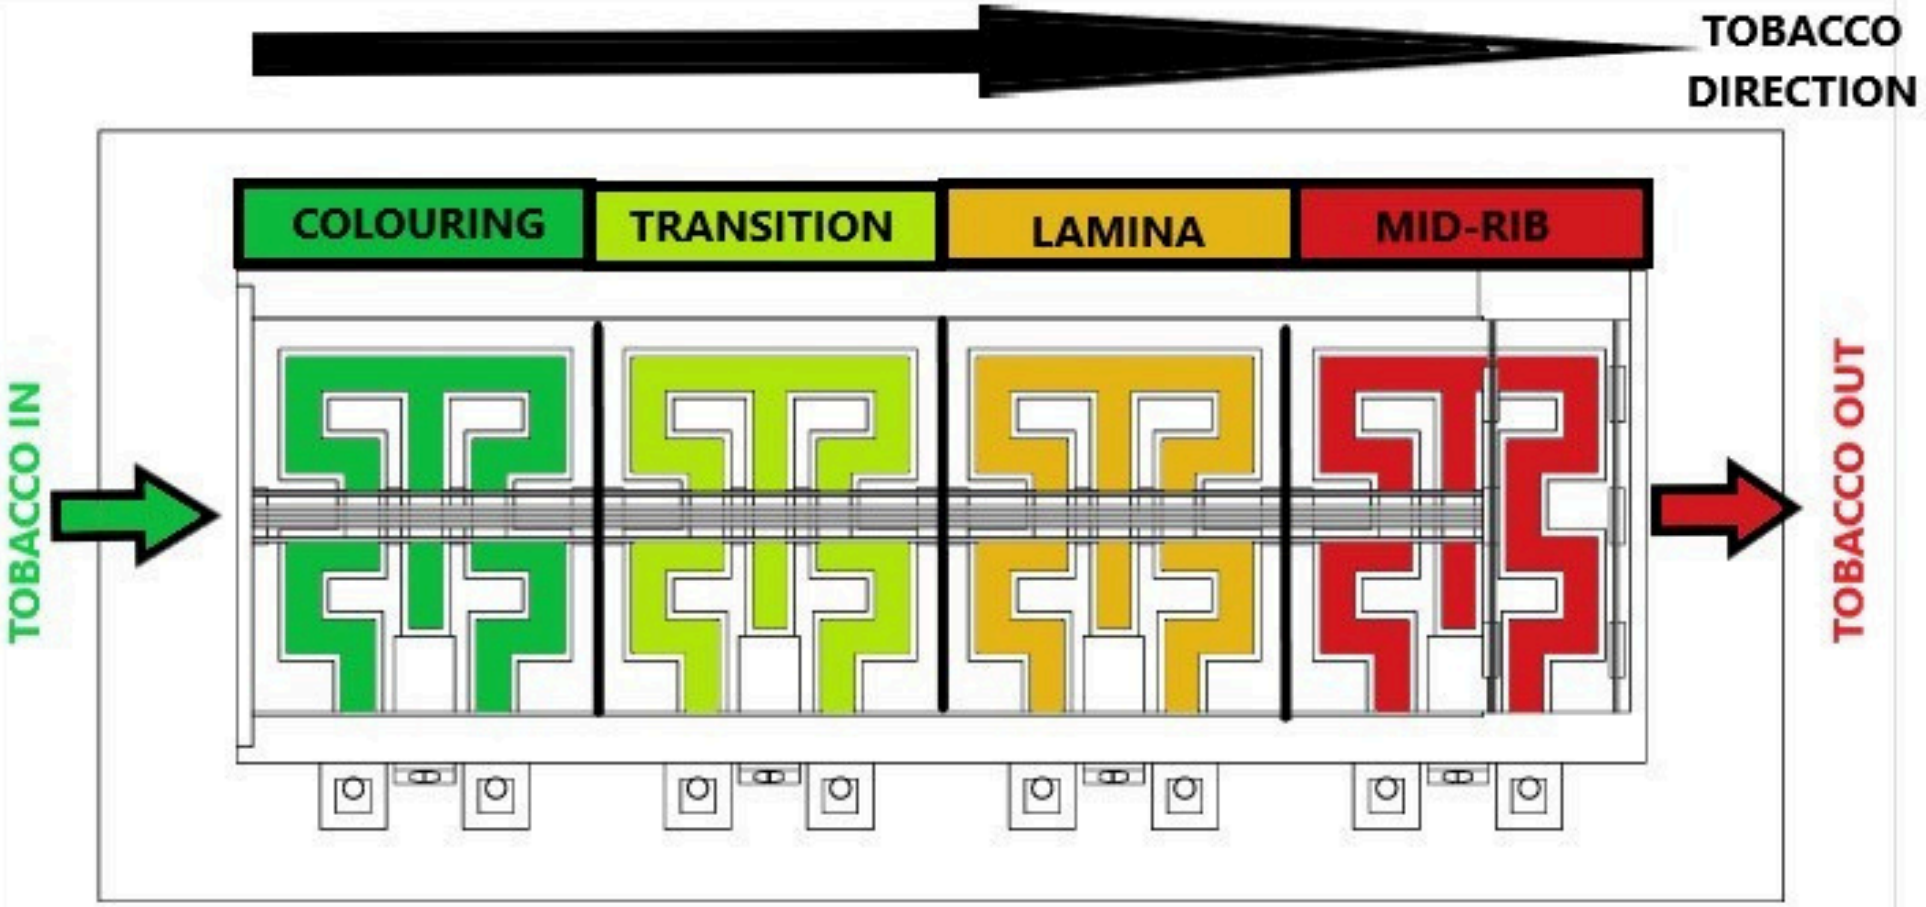


TITLE: 6-HA ROCKET TUNNEL	DESIGNED BY: T.MAGUSHU	DATE: 18/08/25	DRG.No: 1
	CHECKED BY: O.MUDADISI	SCALE: 1:150	SHEET NO: 7
WEIGHT:	APPROVED BY:M.NGWENYA	QTY: 1	SHEET SIZE : A4

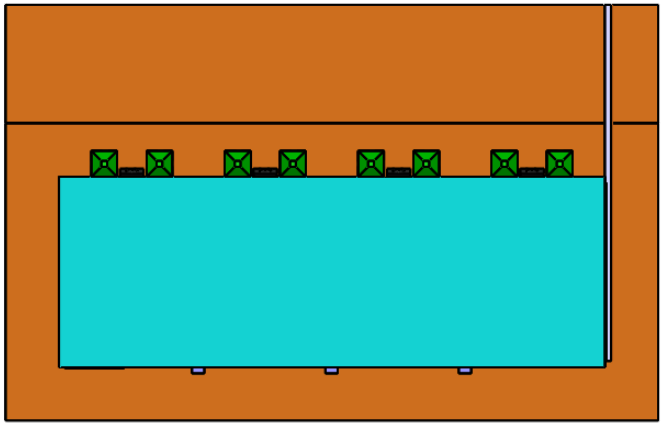


PLAN

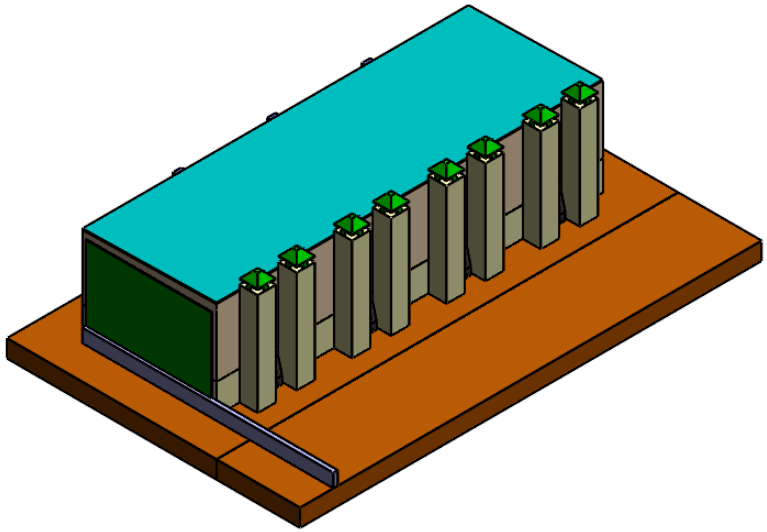


PERSPECTIVE VIEW

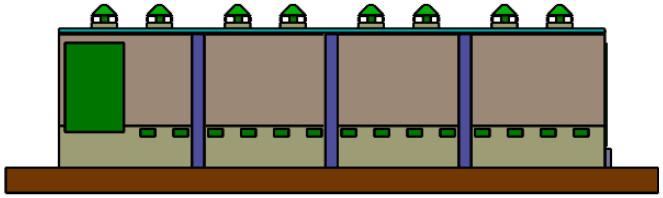


FRONT

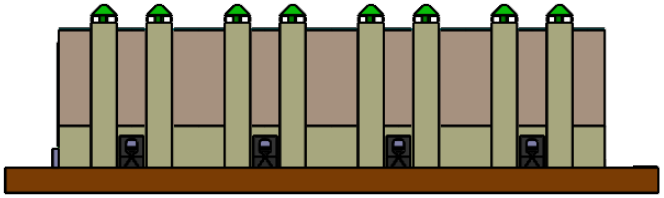


BACK

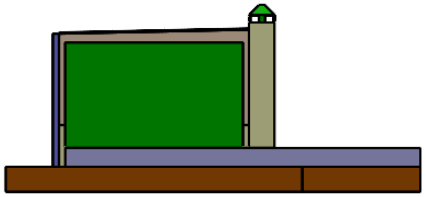

RIGHT SIDE ELEVATION

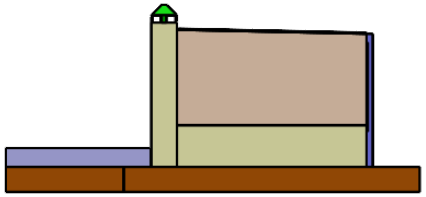


LEFT SIDE ELEVATION

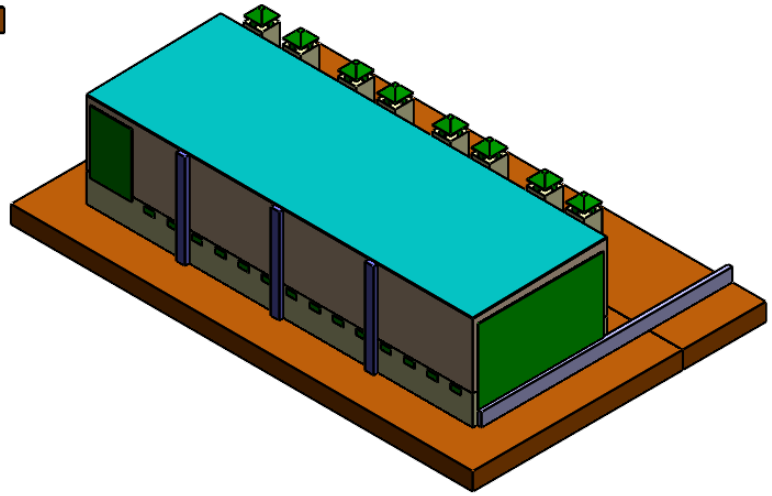

TITLE: 6 HA BARN	DESIGNED Y: T.MAGUSHU	DATE : 31/10/25	DRG. No: 1
	CHECKED BY: O.MUDADISI	SCALE : 1:350	SHEET.No: 1
WEIGHT:	APPROVED Y: M.NGWENYA	QTY : 1	SHEET SIZE : A3

UISAGA
For Productivity. For Sustainability


PLAN

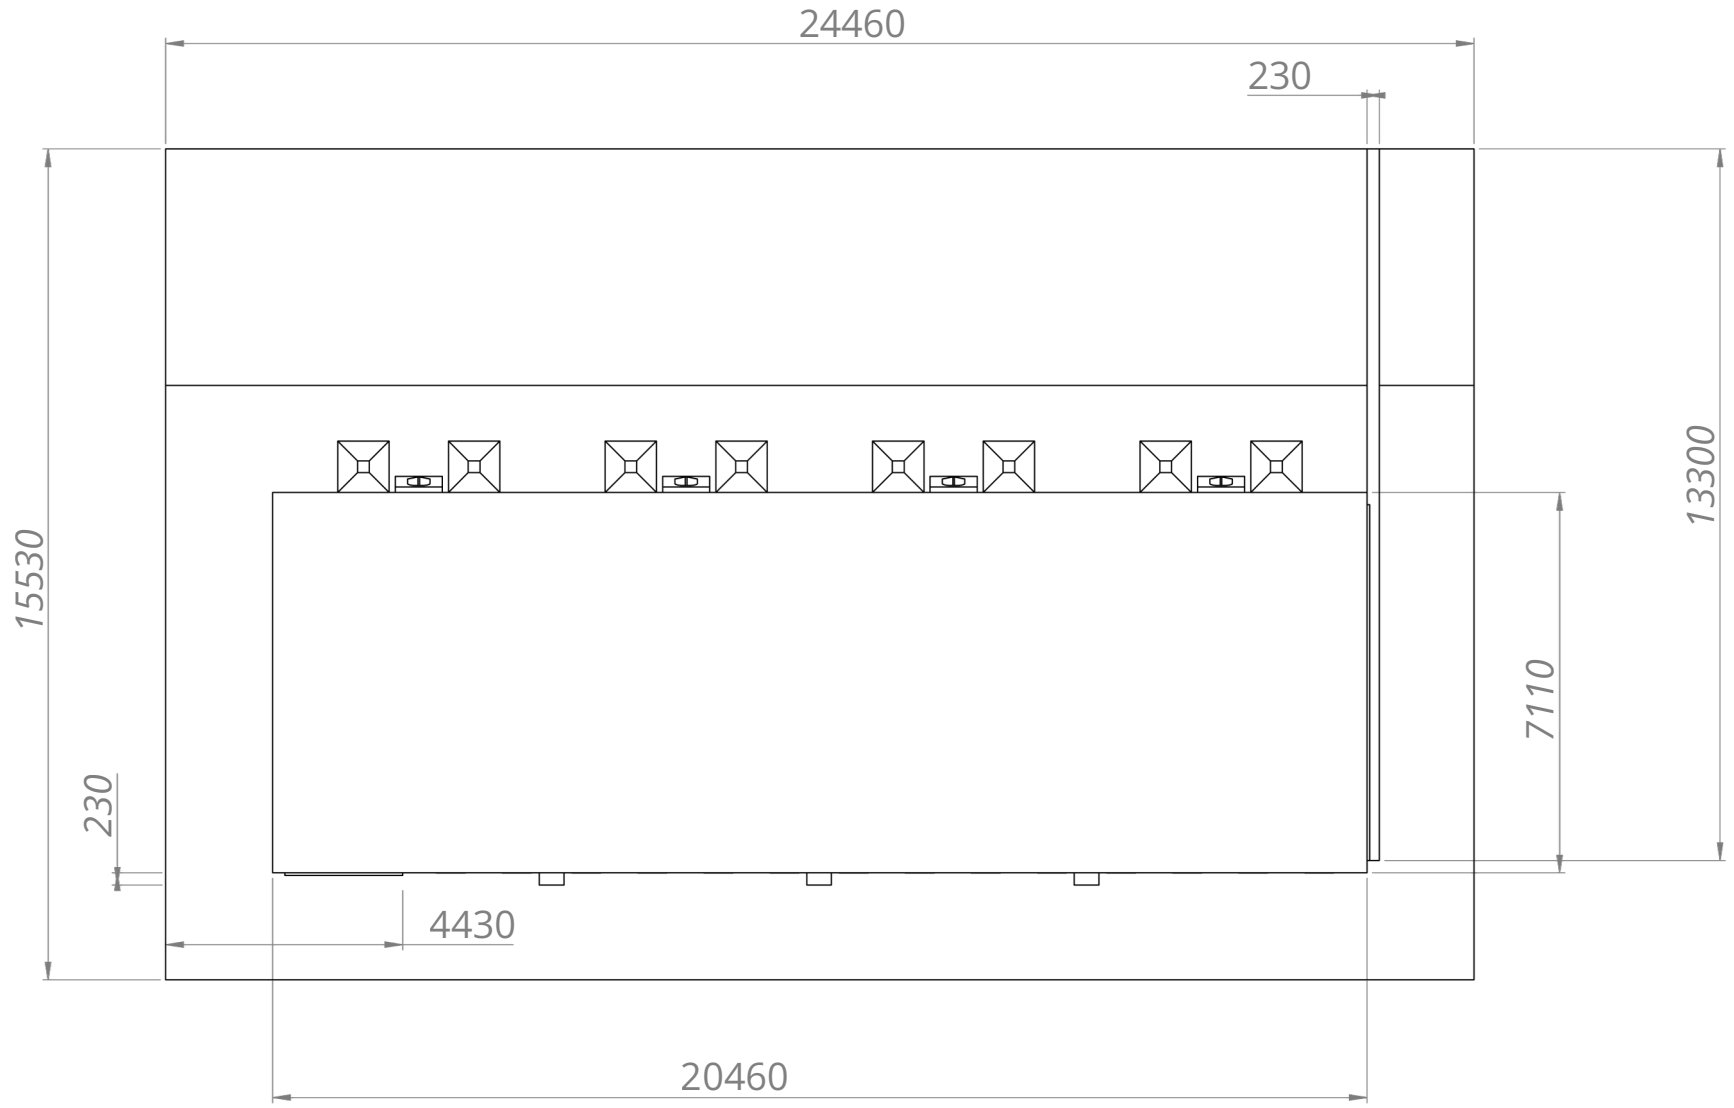


TITLE: 6 HA BARN	DESIGNED Y: T.MAGUSHU	DATE : 31/10/25	DRG. No: 1
	CHECKED BY: O.MUDADISI	SCALE : 1:350	SHEET.No: 2
WEIGHT:	APPROVED Y: M.NGWENYA	QTY : 1	SHEET SIZE : A3

KUISAGA For Productivity. For Sustainability

PLAN

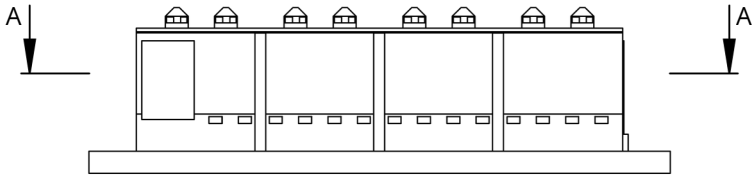

SECTION A-A
SCALE 1 : 100

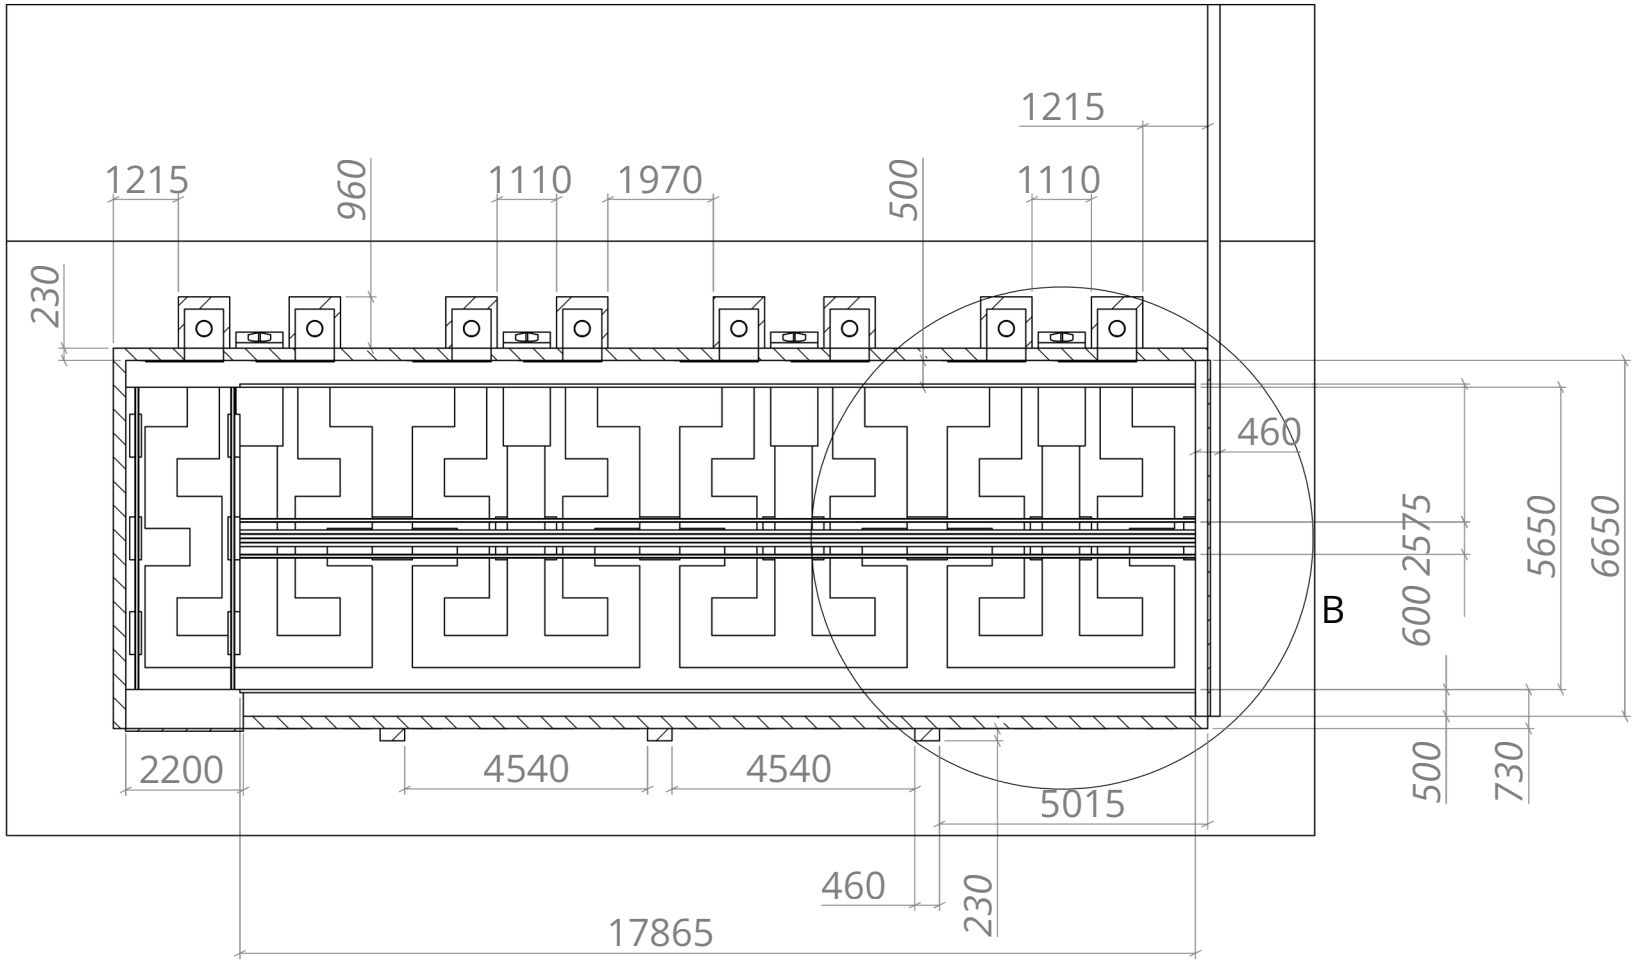


RIGHT SIDE ELEVATION

TITLE: 6 HA BARN	DESIGNED Y: T.MAGUSHU	DATE : 31/10/25	DRG. No: 1
	CHECKED BY: O.MUDADISI	SCALE : 1:350	SHEET.No: 3
WEIGHT:	APPROVED Y: M.NGWENYA	QTY : 1	SHEET SIZE : A3

KUISAGA
For Productivity. For Sustainability

PLAN

DETAIL B
SCALE 1 : 35

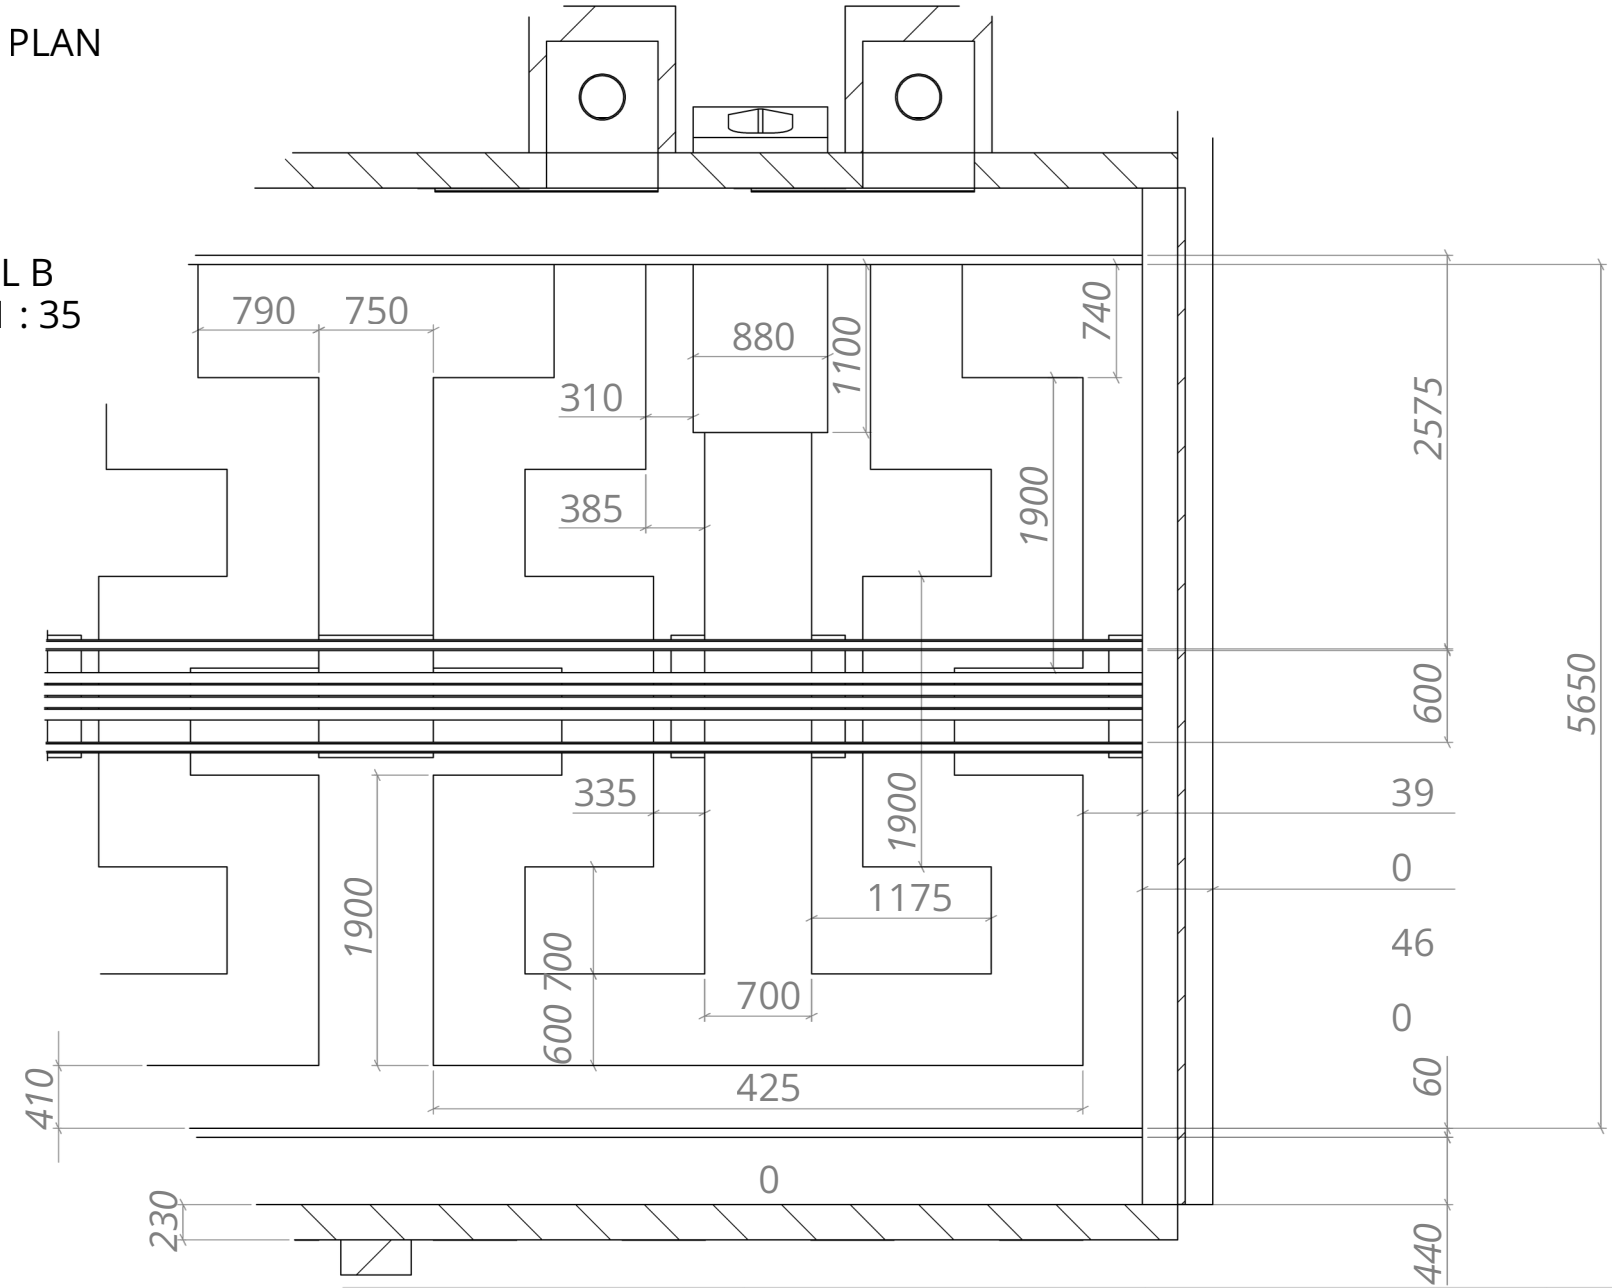


RIGHT SIDE ELEVATION

TITLE: 6 HA BARN	DESIGNED Y: T.MAGUSHU	DATE : 31/10/25	DRG. No: 1
	CHECKED BY: O.MUDADISI	SCALE : 1:350	SHEET.No: 4
WEIGHT:	APPROVED Y: M.NGWENYA	QTY : 1	SHEET SIZE : A3


KUISAGA
For Productivity. For Sustainability

FRONT AND BACK

FRONT

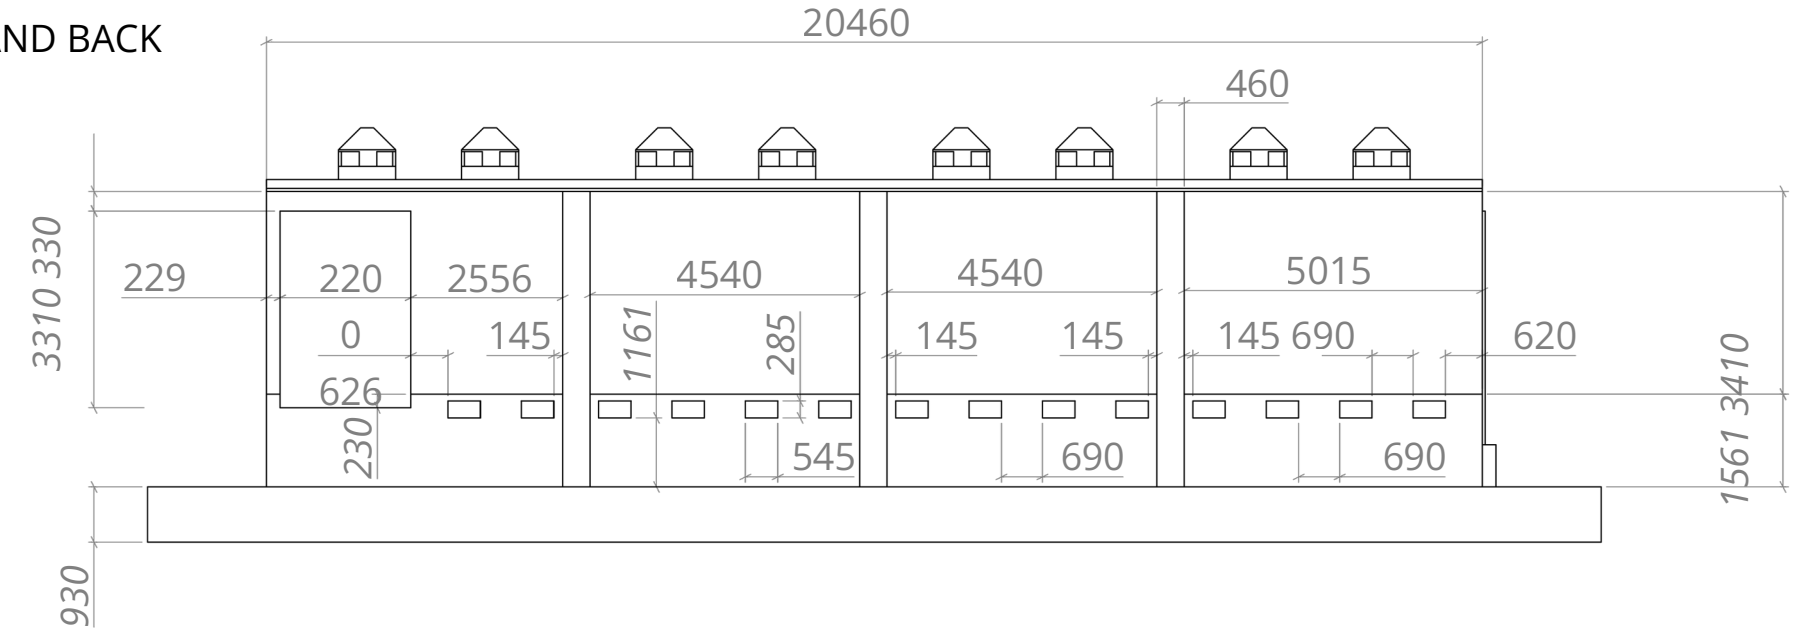


BACK

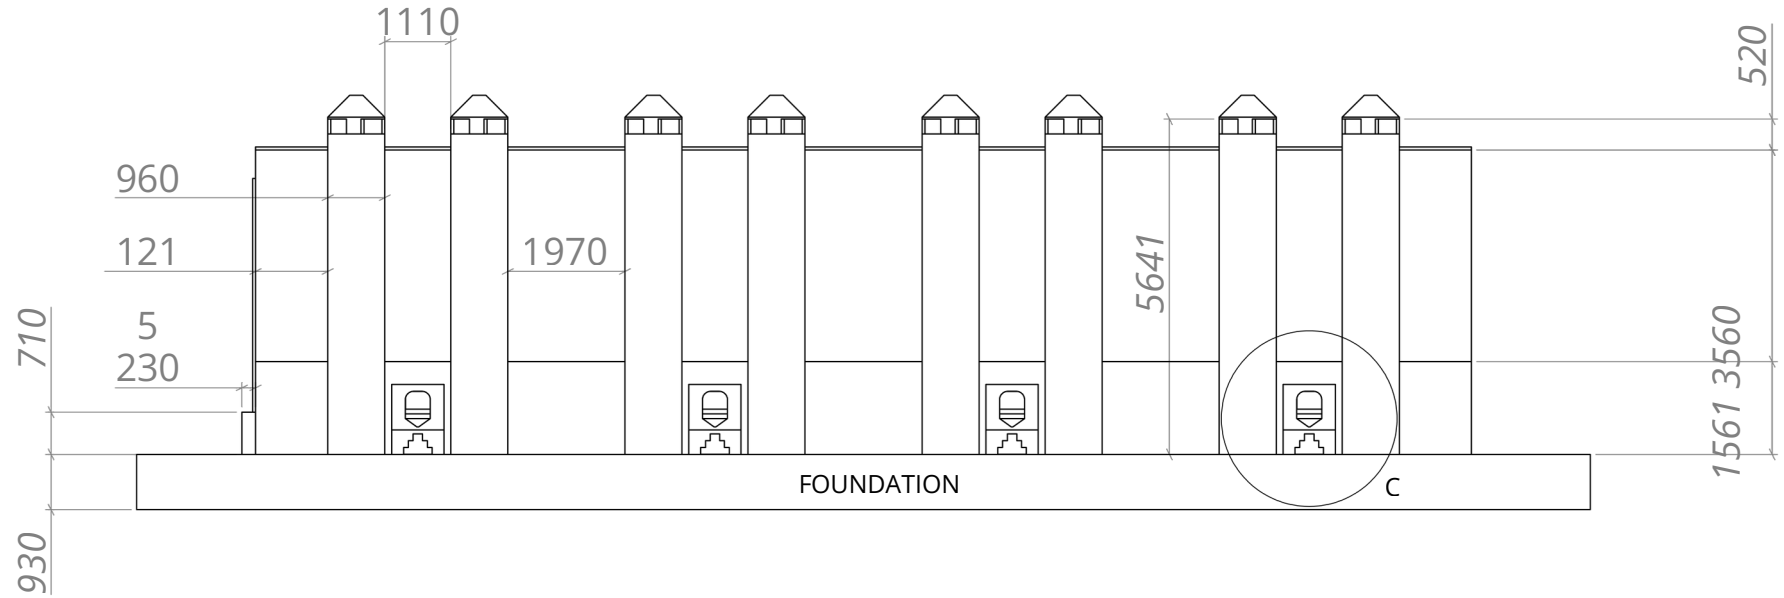


TITLE: 6 HA BARN	DESIGNED Y: T.MAGUSHU	DATE : 31/10/25	DRG. No: 1
	CHECKED BY: O.MUDADISI	SCALE : 1:350	SHEET.No: 5
WEIGHT:	APPROVED Y: M.NGWENYA	QTY : 1	SHEET SIZE : A3

KUISAGA For Productivity. For Sustainability


FURNACE

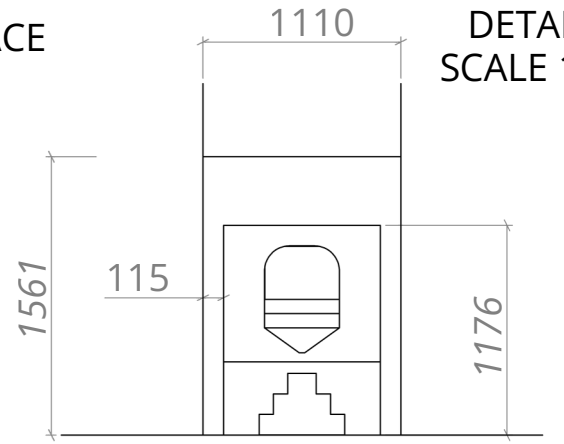


DETAIL C
SCALE 1 : 30

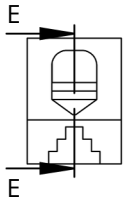


SIDE SECTION

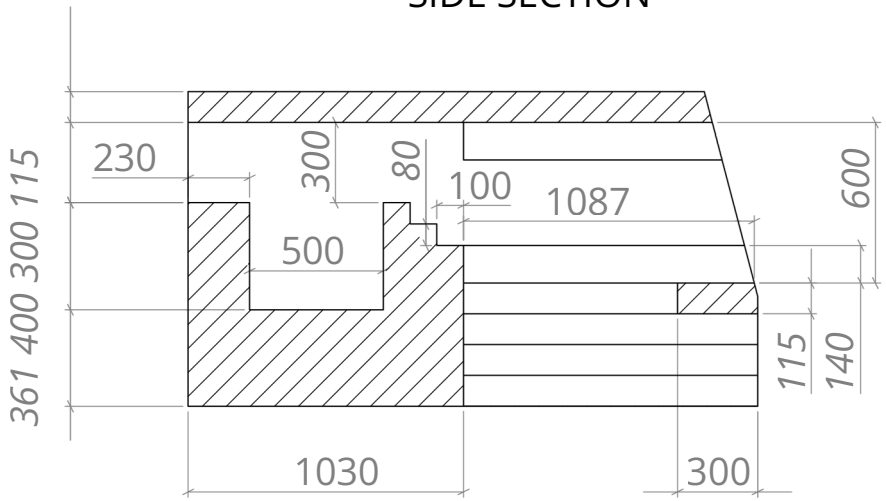


SECTION E-E
SCALE 1 : 20

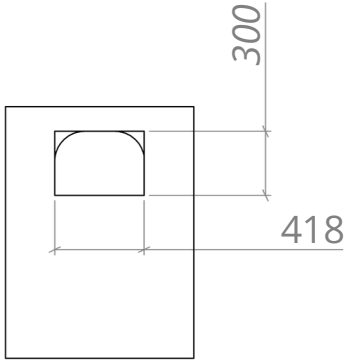

BACK

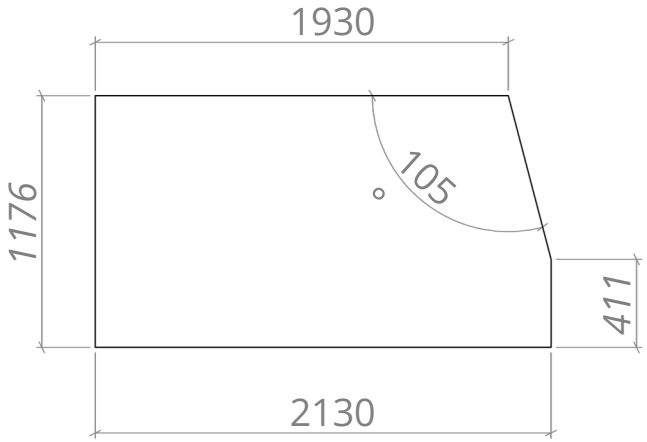

SIDE

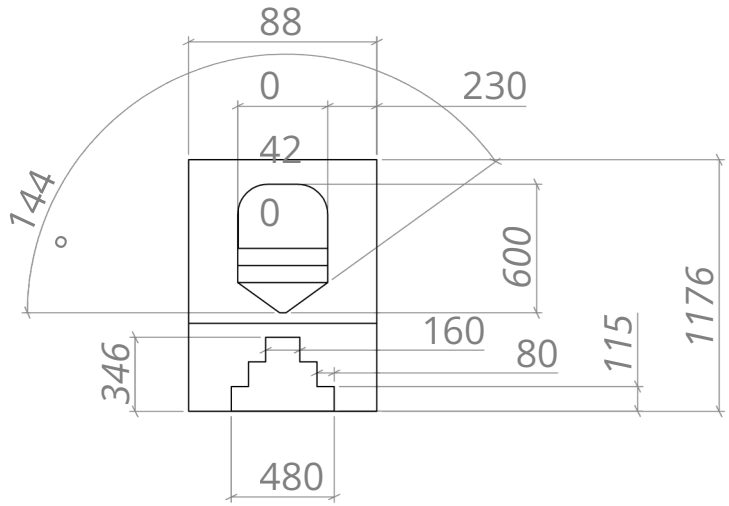



FRONT


TITLE: 6 HA BARN	DESIGNED Y: T.MAGUSHU	DATE : 31/10/25	DRG. No: 1
	CHECKED BY: O.MUDADISI	SCALE : 1:350	SHEET.No: 6
WEIGHT:	APPROVED Y: M.NGWENYA	QTY : 1	SHEET SIZE : A3

KUISAGA
For Productivity. For Sustainability

RIGHT SIDES FROM BARN FRONT

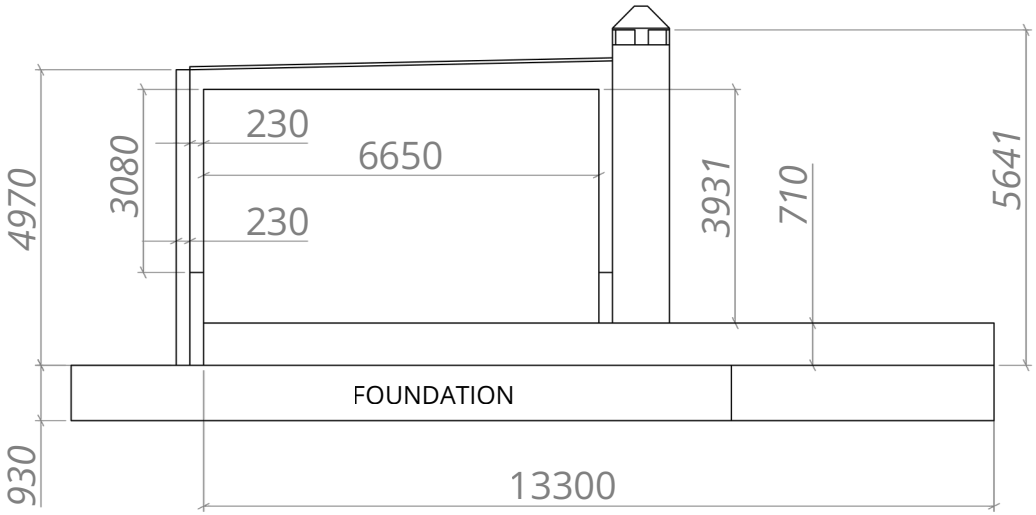

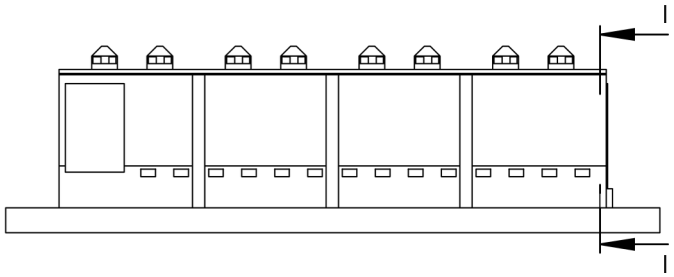


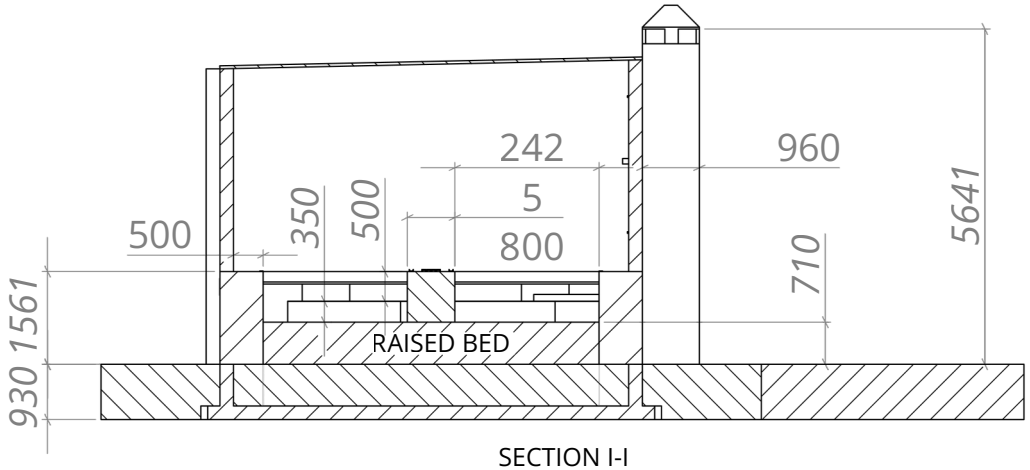


SECTION I-I
SCALE 1 : 90


TITLE: 6 HA BARN	DESIGNED Y: T.MAGUSHU	DATE : 31/10/25	DRG. No: 1
	CHECKED BY: O.MUDADISI	SCALE : 1:350	SHEET.No: 7
WEIGHT:	APPROVED Y: M.NGWENYA	QTY : 1	SHEET SIZE : A3


OUTLET VENTS

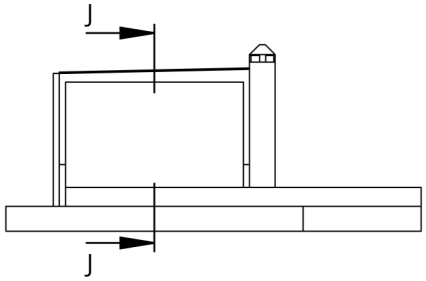

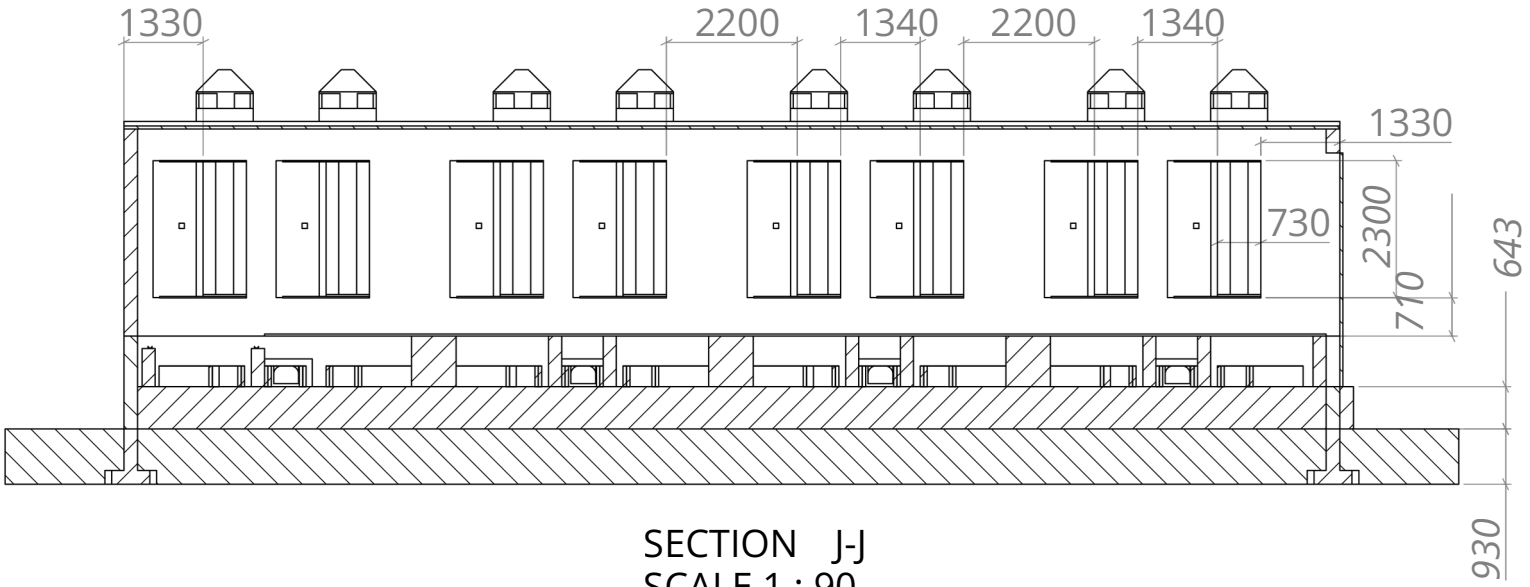

SECTION J-J
SCALE 1 : 90

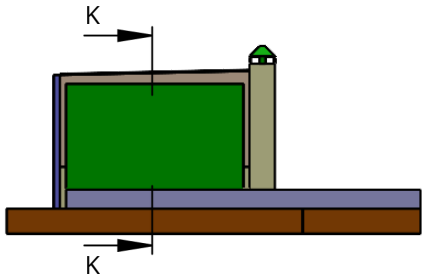

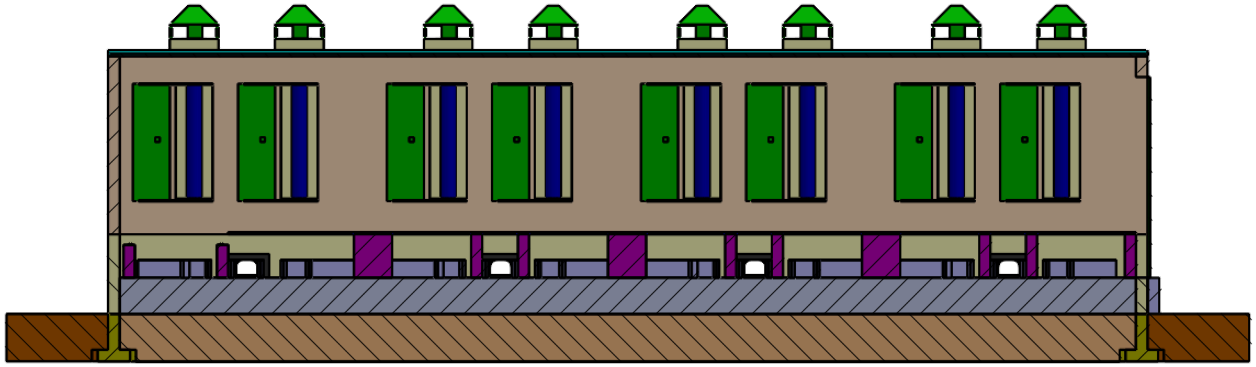



SECTION K-K
SCALE 1 : 105


TITLE: 6 HA BARN	DESIGNED Y: T.MAGUSHU	DATE : 31/10/25	DRG. No: 1
	CHECKED BY: O.MUDADISI	SCALE : 1:350	SHEET.No: 8
WEIGHT:	APPROVED Y: M.NGWENYA	QTY : 1	SHEET SIZE : A3

KUISAGA
For Productivity. For Sustainability

CHIMNEY

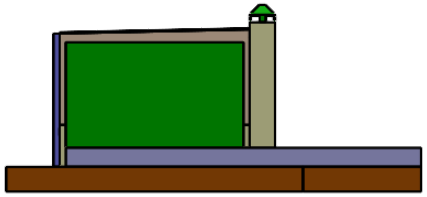

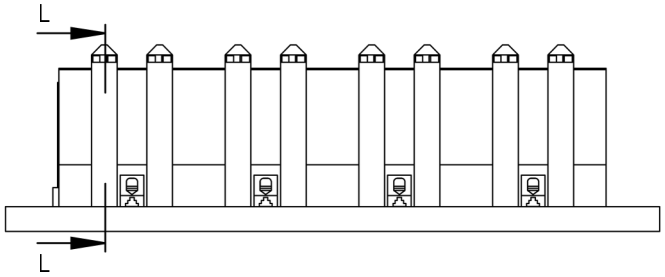

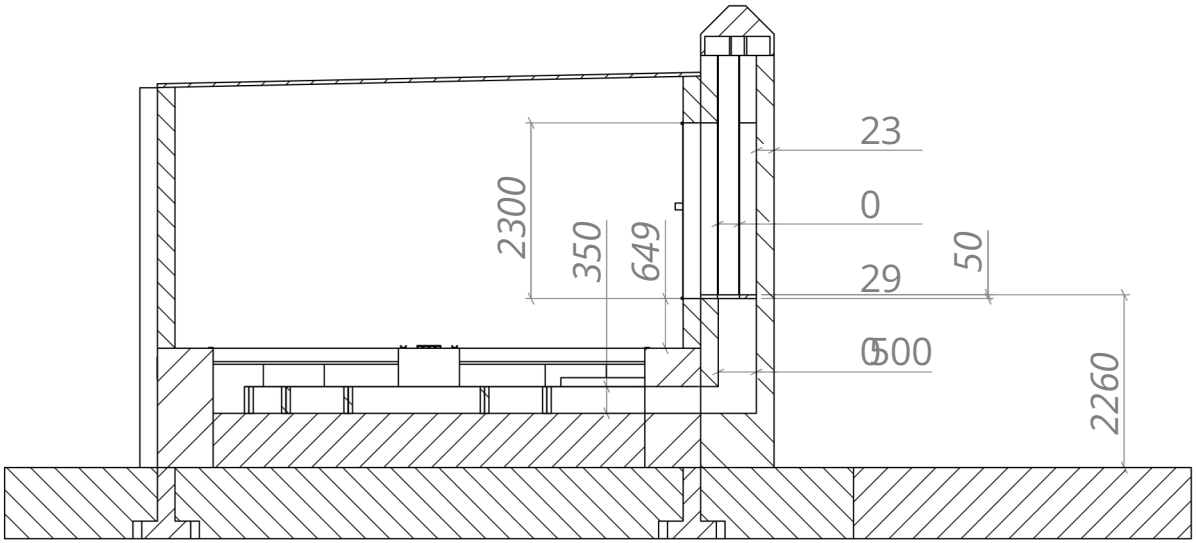

SECTION L-L
SCALE 1 : 70

TITLE: 6 HA BARN	DESIGNED Y: T.MAGUSHU	DATE : 31/10/25	DRG. No: 1
	CHECKED BY: O.MUDADISI	SCALE : 1:350	SHEET.No: 9
WEIGHT:	APPROVED Y: M.NGWENYA	QTY : 1	SHEET SIZE : A3

KUISAGA For Productivity. For Sustainability